

경기도 파주시 탄현면 도시개발사업 신축공사

A r t i s t i c T e c h n o l o g y

2026.07

설계개요 (1단지)

사 업 명			경기도 파주시 탄현면 도시개발사업 신축공사				
대 지 현 황	대 지 위 치		경기도 파주시 탄현면 축현리 608-5번지 일원				
	대 지 면 적	구 역 면 적		74,356.00㎡			
		공제부지					
			소 계				
실사용부지		74,356.00㎡					
지 역 지 구		도시지역, 자연녹지지역 (지구단위계획 수립예정)					
건 물 규 모	구 분		공동주택 및 부대시설				
	구 조		철근 콘크리트조				
	층 수		지하2층 ~ 지상29층				
	건 물 높 이		83.95M				
	건 축 면 적		16,380.00㎡				
	건 폐 율		22.03%				
	지상연면적		154,721.58㎡				
	지하연면적		74,825.40㎡				
	연 면 적		229,546.98㎡				
	용 적 률		208.08%				
	조경면적		24,537.48㎡				
	주 차 대 수	지상	시행 11.0대		공동주택	근린생활시설	계
		지하	시행 2,036대		법정 1,634.21대	법정 4.95대	법정 1,639.16대
계		시행 2,047대		세대당 1.45대			
기 타 내 용		* 상기개요는 각종심의등 인허가시 변경될수도 있음					

공동 주택 분양 면적표

구 분		세대수	비율 (%)	전용면적	주 거 공 용 면 적			공급면적	기 타 공 용 면 적			계약면적
					벽체공유	계단, 홀	소 계		관리,경비,부대시설등	지하주차장	소 계	
일반분양		0	0.00%	0.00㎡	0.00㎡	0.00㎡	0.00㎡	0.00㎡	0.00㎡	0.00㎡	0.00㎡	0.00㎡
	59-A형	149	10.55%	59.97㎡	6.62㎡	15.34㎡	21.96㎡	81.93㎡	1.43㎡	38.94㎡	40.37㎡	122.30㎡
	59-B형	104	7.37%	59.98㎡	6.67㎡	15.34㎡	22.01㎡	81.99㎡	1.43㎡	38.95㎡	40.38㎡	122.37㎡
	74-A형	203	14.38%	74.97㎡	7.72㎡	19.17㎡	26.89㎡	101.86㎡	1.79㎡	48.68㎡	50.47㎡	152.33㎡
	84-A형	468	33.14%	84.97㎡	7.76㎡	21.73㎡	29.49㎡	114.46㎡	2.03㎡	55.17㎡	57.20㎡	171.66㎡
	84-B형	438	31.02%	84.98㎡	7.79㎡	21.73㎡	29.52㎡	114.50㎡	2.03㎡	55.18㎡	57.21㎡	171.71㎡
	110형	50	3.54%	110.42㎡	9.84㎡	28.24㎡	38.08㎡	148.50㎡	2.63㎡	71.70㎡	74.33㎡	222.83㎡
			0.00%	0.00㎡	0.00㎡	0.00㎡	0.00㎡	0.00㎡	0.00㎡	0.00㎡	0.00㎡	0.00㎡
합 계		1,412	100.00%	112,900.56㎡	10,782.92㎡	28,870.00㎡	39,652.92㎡	152,553.48㎡	2,693.10㎡	73,310.40㎡	76,003.50㎡	228,556.98㎡

부대 복리시설 개요

구 분		법 정 면 적		계획면적
부 대 시 설 및 복 리 시 설	진 입 도 로	1000 세대 이상	= 12M이상	20M
	단지내 도 로	10M 이상	= 10M	10M
	관 리 사 무 소	10 + (세대수 - 50) X 0.05	= 78.10㎡	358.10㎡
	저 수 조	(세대수 X 0.5t) +20t	= 726 t	726 t
	근린생활시설			990.00㎡
	주민운동시설			627.00㎡
	경 로 당			375.00㎡
	임주자공동시설			1,065.00㎡
	어린이집			330.00㎡
	어린이놀이터			990.00㎡
	작은도서관			65.00㎡
		(주민공동시설: 500+세대당2.0㎡ 이상)	3,324.00㎡	3,452.00㎡

용도별 면적

구 분	지상층면적	지하층면적	합 계	비 고
공동주택 (아파트)	152,553.48㎡	-	152,553.48㎡	
근린생활시설	990.00㎡		990.00㎡	
부대복리시설	1,128.10㎡	1,065.00㎡	2,193.10㎡	
경 비 실	50.00㎡	-	50.00㎡	
전기,발전기실및기계실	-	450.00㎡	450.00㎡	
지하 주차장	-	73,310.40㎡	73,310.40㎡	
계	154,721.58㎡	74,825.40㎡	229,546.98㎡	

설계개요 (2단지)

사 업 명			경기도 파주시 탄현면 도시개발사업 신축공사				
대 지 현 황	대 지 위 치		경기도 파주시 탄현면 축현리 608-5번지 일원				
	대 지 면 적	구 역 면 적		31,339.00㎡			
		공제부지					
			소 계				
실사용부지		31,339.00㎡					
지 역 지 구		도시지역, 자연녹지지역 (지구단위계획 수립예정)					
건 물 규 모	구 분		공동주택 및 부대시설				
	구 조		철근 콘크리트조				
	층 수		지하2층 ~ 지상29층				
	건 물 높 이		84				
	건 축 면 적		7,180.00㎡				
	건 폐 율		22.91%				
	지상연면적		72,022.34㎡				
	지하연면적		35,039.20㎡				
	연 면 적		107,061.54㎡				
	용 적 률		229.82%				
	조경면적		10,341.87㎡				
	주 차 대 수	지상	시행 10.0대		공동주택	근린생활시설	계
		지하	시행 941대		법정 757.36대	법정 2.10대	법정 759.46대
계		시행 951대		세대당 1.45대			
기 타 내 용		* 상기개요는 각종심의등 인허가시 변경될수도 있음					

공동 주택 분양 면적표

구 분		세대수	비율 (%)	전용면적	주 거 공 용 면 적			공급면적	기 타 공 용 면 적			계약면적
					벽체공유	계단, 홀	소 계		관리,경비,부대시설등	지하주차장	소 계	
일반분양		0	0.00%	0.00㎡	0.00㎡	0.00㎡	0.00㎡	0.00㎡	0.00㎡	0.00㎡	0.00㎡	0.00㎡
	59-A형	70	10.67%	59.97㎡	6.62㎡	15.10㎡	21.72㎡	81.69㎡	2.66㎡	38.84㎡	41.50㎡	123.19㎡
	59-B형	52	7.93%	59.98㎡	6.67㎡	15.10㎡	21.77㎡	81.75㎡	2.66㎡	38.85㎡	41.50㎡	123.26㎡
	74-A형	38	5.79%	74.97㎡	7.72㎡	18.87㎡	26.59㎡	101.56㎡	3.32㎡	48.56㎡	51.88㎡	153.44㎡
	84-A형	280	42.68%	84.97㎡	7.76㎡	21.39㎡	29.15㎡	114.12㎡	3.76㎡	55.04㎡	58.80㎡	172.92㎡
	84-B형	216	32.93%	84.98㎡	7.79㎡	21.39㎡	29.18㎡	114.16㎡	3.76㎡	55.04㎡	58.80㎡	172.97㎡
			0.00%	0.00㎡	0.00㎡	0.00㎡	0.00㎡	0.00㎡	0.00㎡	0.00㎡	0.00㎡	0.00㎡
			0.00%	0.00㎡	0.00㎡	0.00㎡	0.00㎡	0.00㎡	0.00㎡	0.00㎡	0.00㎡	0.00㎡
합 계		656	100.00%	52,313.00㎡	4,959.04㎡	13,170.00㎡	18,129.04㎡	70,442.04㎡	2,316.30㎡	33,883.20㎡	36,199.50㎡	106,641.54㎡

부대 복리시설 개요

구 분		법 정 면 적		계 획 면 적
부 대 시 설 및 복 리 시 설	진 입 도 로	1000 세대 이상	= 12M이상	20M
	단지내 도 로	10M 이상	= 10M	10M
	관 리 사 무 소	10 + (세대수 - 50) X 0.05	= 40.30㎡	340.30㎡
	저 수 조	(세대수 X 0.5t) +20t	= 348 t	348 t
	근린생활시설			420.00㎡
	주민운동시설			427.00㎡
	경 로 당			375.00㎡
	임주자공동시설			706.00㎡
	어린이집			330.00㎡
	어린이놀이터			690.00㎡
	작은도서관			65.00㎡
		(주민공동시설: 세대당2.5㎡ 이상)	1,640.00㎡	2,593.00㎡

용도별 면적

구 분	지상층면적	지하층면적	합 계	비 고
공동주택 (아파트)	70,442.04㎡	-	70,442.04㎡	
근린생활시설	420.00㎡		420.00㎡	
부대복리시설	1,110.30㎡	706.00㎡	1,816.30㎡	
경 비 실	50.00㎡	-	50.00㎡	
전기,발전기실및기계실	-	450.00㎡	450.00㎡	
지하 주차장	-	33,883.20㎡	33,883.20㎡	
계	72,022.34㎡	35,039.20㎡	107,061.54㎡	

설계개요 (3단지)

사 업 명			경기도 파주시 탄현면 도시개발사업 신축공사				
대 지 현 황	대 지 위 치		경기도 파주시 탄현면 축현리 608-5번지 일원				
	대 지 면 적	구 역 면 적		21,486.00㎡			
		공제부지					
		소 계					
실사용부지		21,486.00㎡					
지 역 지 구		도시지역, 자연녹지지역 (지구단위계획 수립예정)					
건 물 규 모	구 분		공동주택 및 부대시설				
	구 조		철근 콘크리트조				
	층 수		지하2층 ~ 지상29층				
	건 물 높 이		83.95M				
	건 축 면 적		4,890.00㎡				
	건 폐 율		22.76%				
	지상연면적		47,595.76㎡				
	지하연면적		22,485.25㎡				
	연 면 적		70,081.01㎡				
	용 적 륜		221.52%				
	조경면적		7,090.38㎡				
	주 차 대 수	지상	시행 4.0대		공동주택	근린생활시설	계
		지하	시행 615대		법정 496.22대	법정 1.95대	법정 498.17대
		계	시행 619대		세대당 1.45대		
기 타 내 용		* 상기개요는 각종심의등 인허가시 변경될수도 있음					

공동 주택 분양 면적표


구 분		세대수	비율 (%)	전용면적	주 거 공 용 면 적			공급면적	기 타 공 용 면 적			계약면적
					벽체공유	계단 , 홀	소 계		관리,경비,부대시설등	지하주차장	소 계	
일반분양		0	0.00%	0.00㎡	0.00㎡	0.00㎡	0.00㎡	0.00㎡	0.00㎡	0.00㎡	0.00㎡	0.00㎡
	59-A형	50	11.71%	59.97㎡	6.62㎡	15.29㎡	21.91㎡	81.88㎡	3.46㎡	37.72㎡	41.17㎡	123.05㎡
	59-B형	32	7.49%	59.98㎡	6.67㎡	15.29㎡	21.96㎡	81.94㎡	3.46㎡	37.72㎡	41.18㎡	123.12㎡
			0.00%	0.00㎡	0.00㎡	0.00㎡	0.00㎡	0.00㎡	0.00㎡	0.00㎡	0.00㎡	0.00㎡
	84-A형	201	47.07%	84.97㎡	7.76㎡	21.66㎡	29.42㎡	114.39㎡	4.90㎡	53.44㎡	58.34㎡	172.73㎡
	84-B형	144	33.72%	84.98㎡	7.79㎡	21.67㎡	29.46㎡	114.44㎡	4.90㎡	53.45㎡	58.34㎡	172.78㎡
			0.00%	0.00㎡	0.00㎡	0.00㎡	0.00㎡	0.00㎡	0.00㎡	0.00㎡	0.00㎡	0.00㎡
			0.00%	0.00㎡	0.00㎡	0.00㎡	0.00㎡	0.00㎡	0.00㎡	0.00㎡	0.00㎡	0.00㎡
합 계		427	100.00%	34,233.95㎡	3,225.96㎡	8,728.00㎡	11,953.96㎡	46,187.91㎡	1,973.85㎡	21,530.25㎡	23,504.10㎡	69,692.01㎡

부대 복리시설 개요

구 분		법 정 면 적		계획면적
부 대 시 설 및 복 리 시 설	진 입 도 로	1000 세대 이상	= 12M이상	20M
	단지내 도 로	10M 이상	= 10M	10M
	관 리 사 무 소	10 + (세대수 - 50) X 0.05	= 28.85㎡	308.85㎡
	저 수 조	(세대수 X 0.5t) +20t	= 234 t	234 t
	근린생활시설			389.00㎡
	주민운동시설			327.00㎡
	경 로 당			315.00㎡
	임주자공동시설			505.00㎡
	어린이집			300.00㎡
	어린이놀이터			600.00㎡
	작은도서관			45.00㎡
		(주민공동시설:세대당2.5㎡ 이상)	1,067.50㎡	2,092.00㎡

용도별 면적

구 분	지상층면적	지하층면적	합 계	비 고
공동주택 (아파트)	46,187.91㎡	-	46,187.91㎡	
근린생활시설	389.00㎡		389.00㎡	
부대복리시설	968.85㎡	505.00㎡	1,473.85㎡	
경 비 실	50.00㎡	-	50.00㎡	
전기,발전기실및기계실	-	450.00㎡	450.00㎡	
지하 주차장	-	21,530.25㎡	21,530.25㎡	
계	47,595.76㎡	22,485.25㎡	70,081.01㎡	

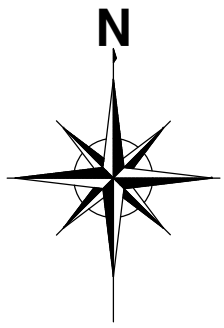

× 6.3

■ 형별세대수 3단지 21,486

구 분	형 별	세 대 수	비 율
	59-A형	50 세대	11.71 %
	59-B형	82 세대	7.49 %
	84-A형	201 세대	47.07 %
	84-B형	144 세대	33.72 %
합 계		427 세대	100.00 %

× 8.5

■ 형별세대수 2단지 31,339

구 분	형 별	세 대 수	비 율
	59-A형	70 세대	10.67 %
	59-B형	52 세대	7.93 %
	74형	38 세대	5.79 %
	84-A형	280 세대	42.68 %
	84-B형	216 세대	32.93 %
합 계		656 세대	100.00 %


■ 형별 전체세대수 1-3단지

구 분	형 별	세 대 수	비 율
	59-A형	269 세대	10.78 %
	59-B형	188 세대	7.54 %
	74형	241 세대	9.66 %
	84-A형	949 세대	38.04 %
	84-B형	798 세대	31.98 %
	110형	50 세대	2.00 %
합 계		2,495세대	100.00 %




■ 형별세대수 1단지 74356


구 분	형 별	세 대 수	비 율
	59-A형	149 세대	10.55 %
	59-B형	104 세대	7.37 %
	74형	203 세대	14.38 %
	84-A형	468 세대	33.14 %
	84-B형	438 세대	31.02 %
	110형	50 세대	3.54 %
합 계		1,412세대	100.00 %

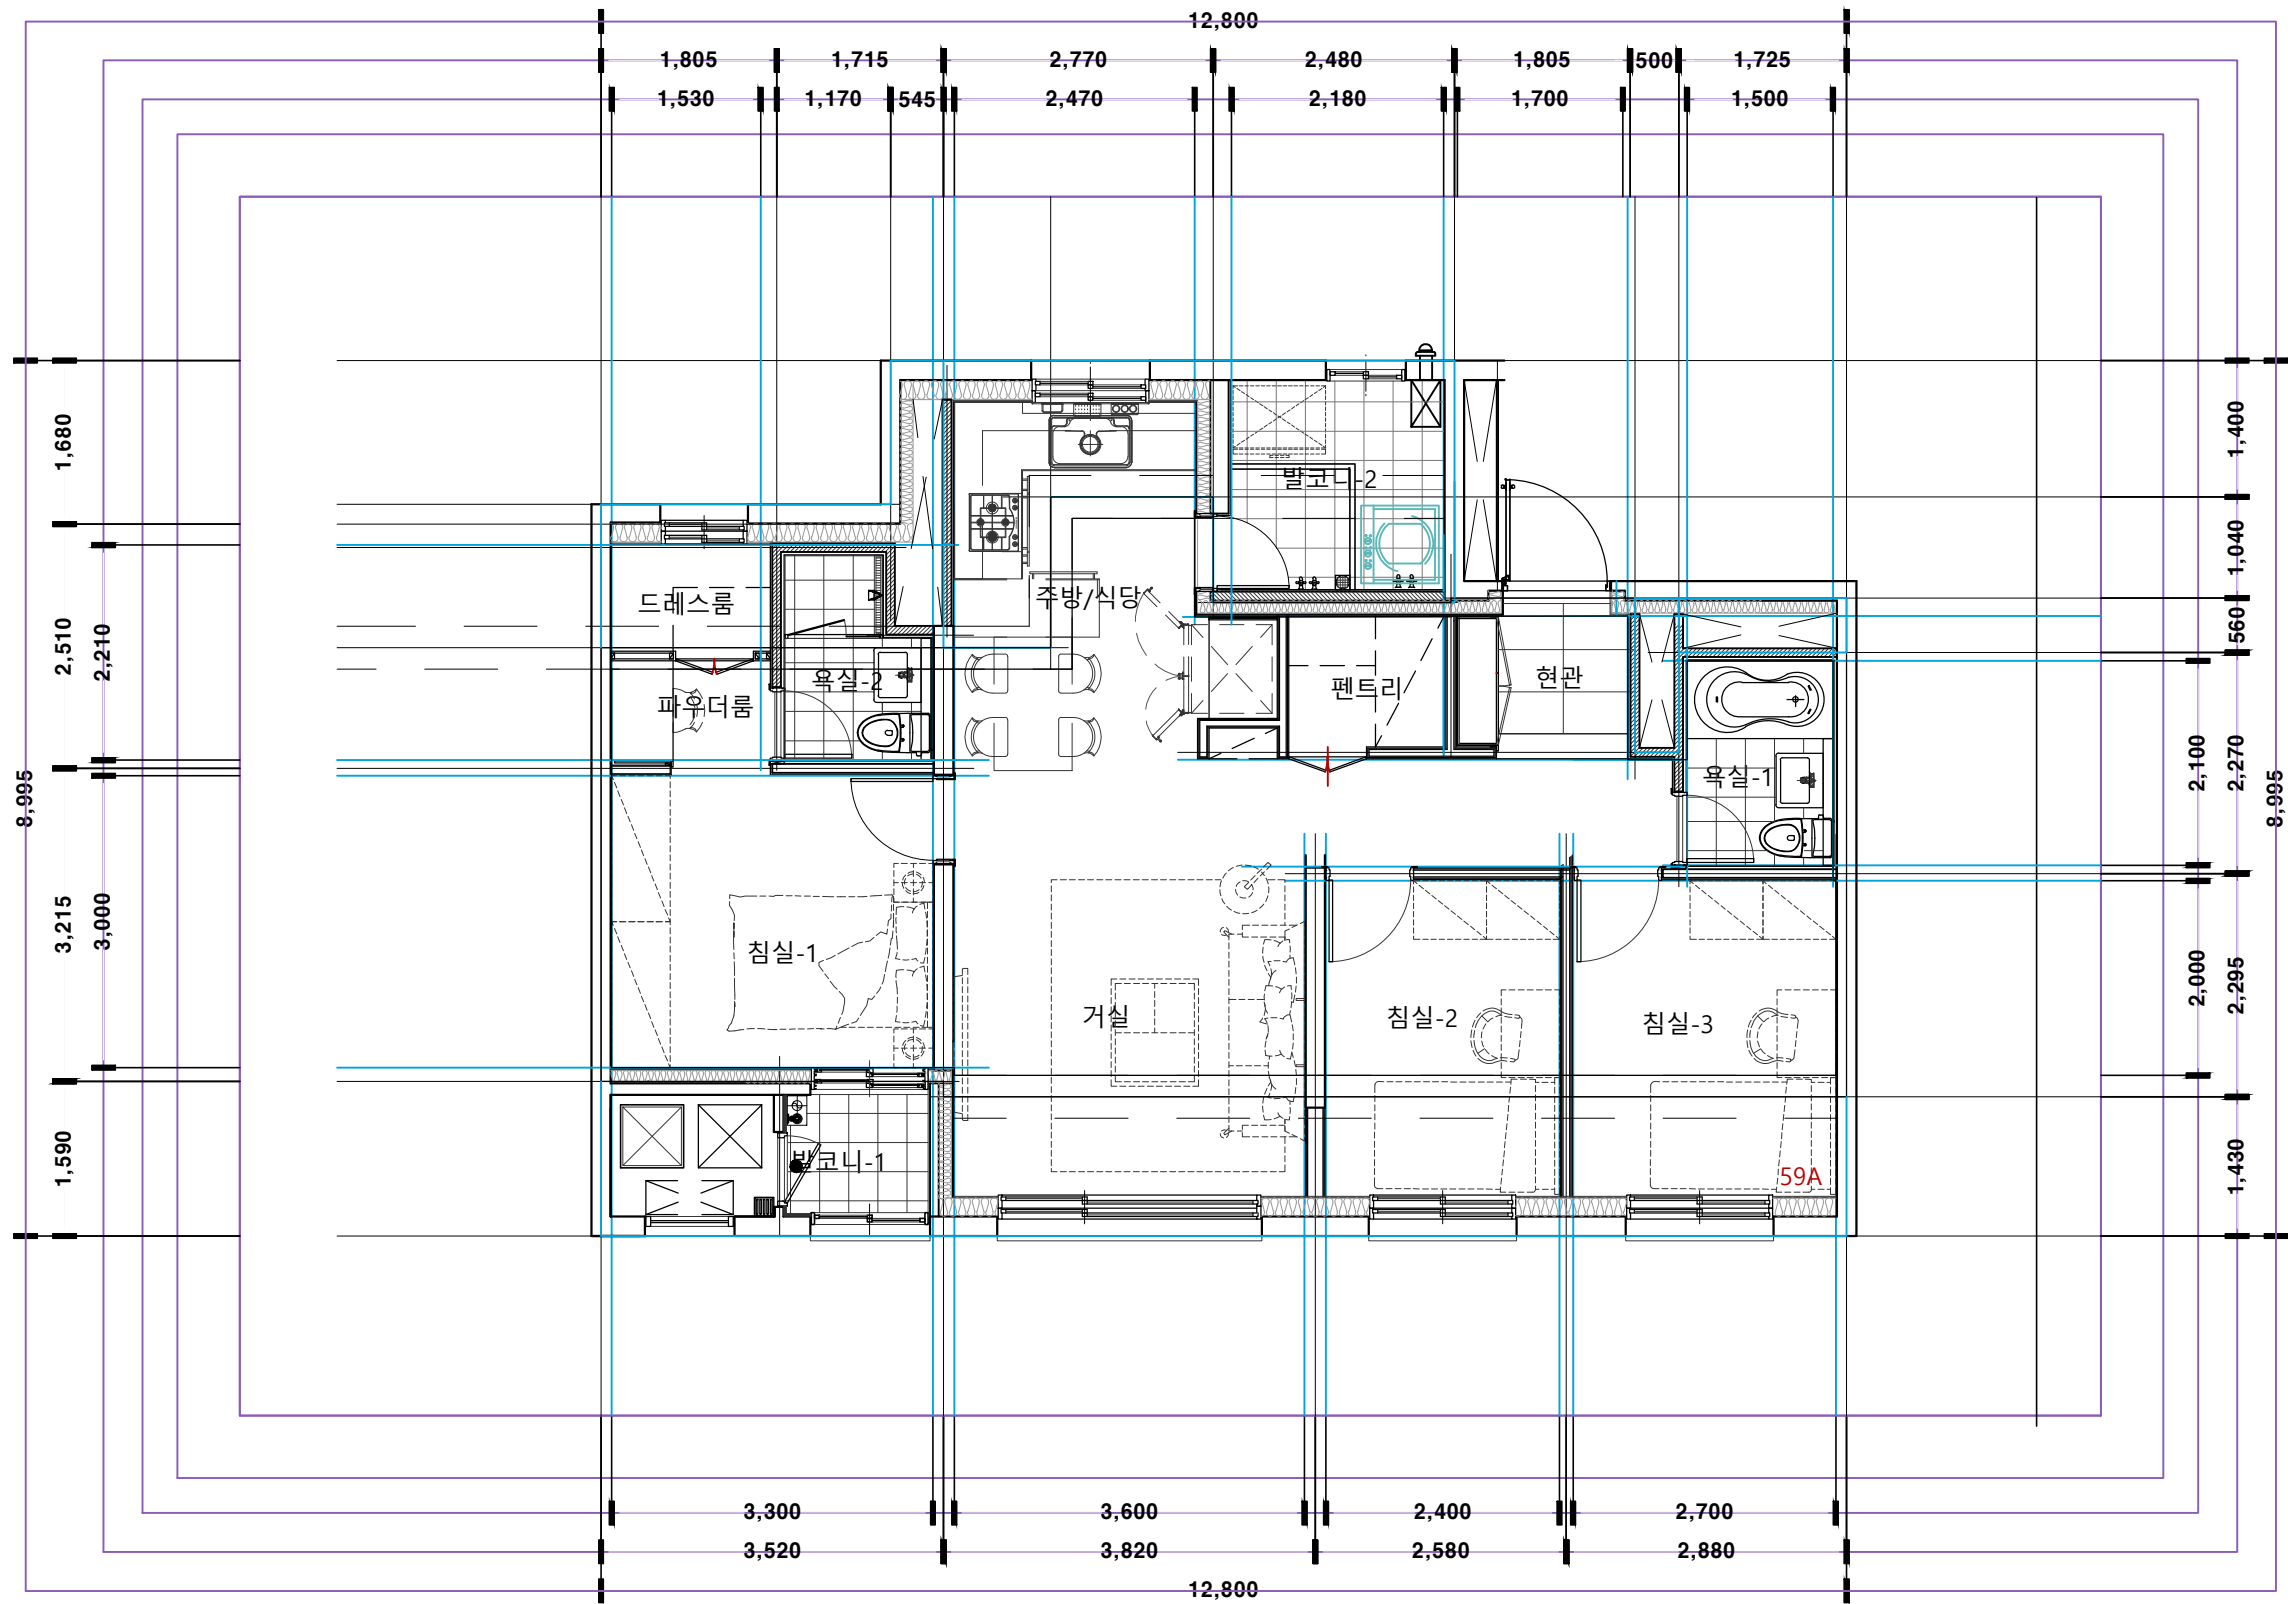


59A-단위세대평면도 SCALE : 1 / 80

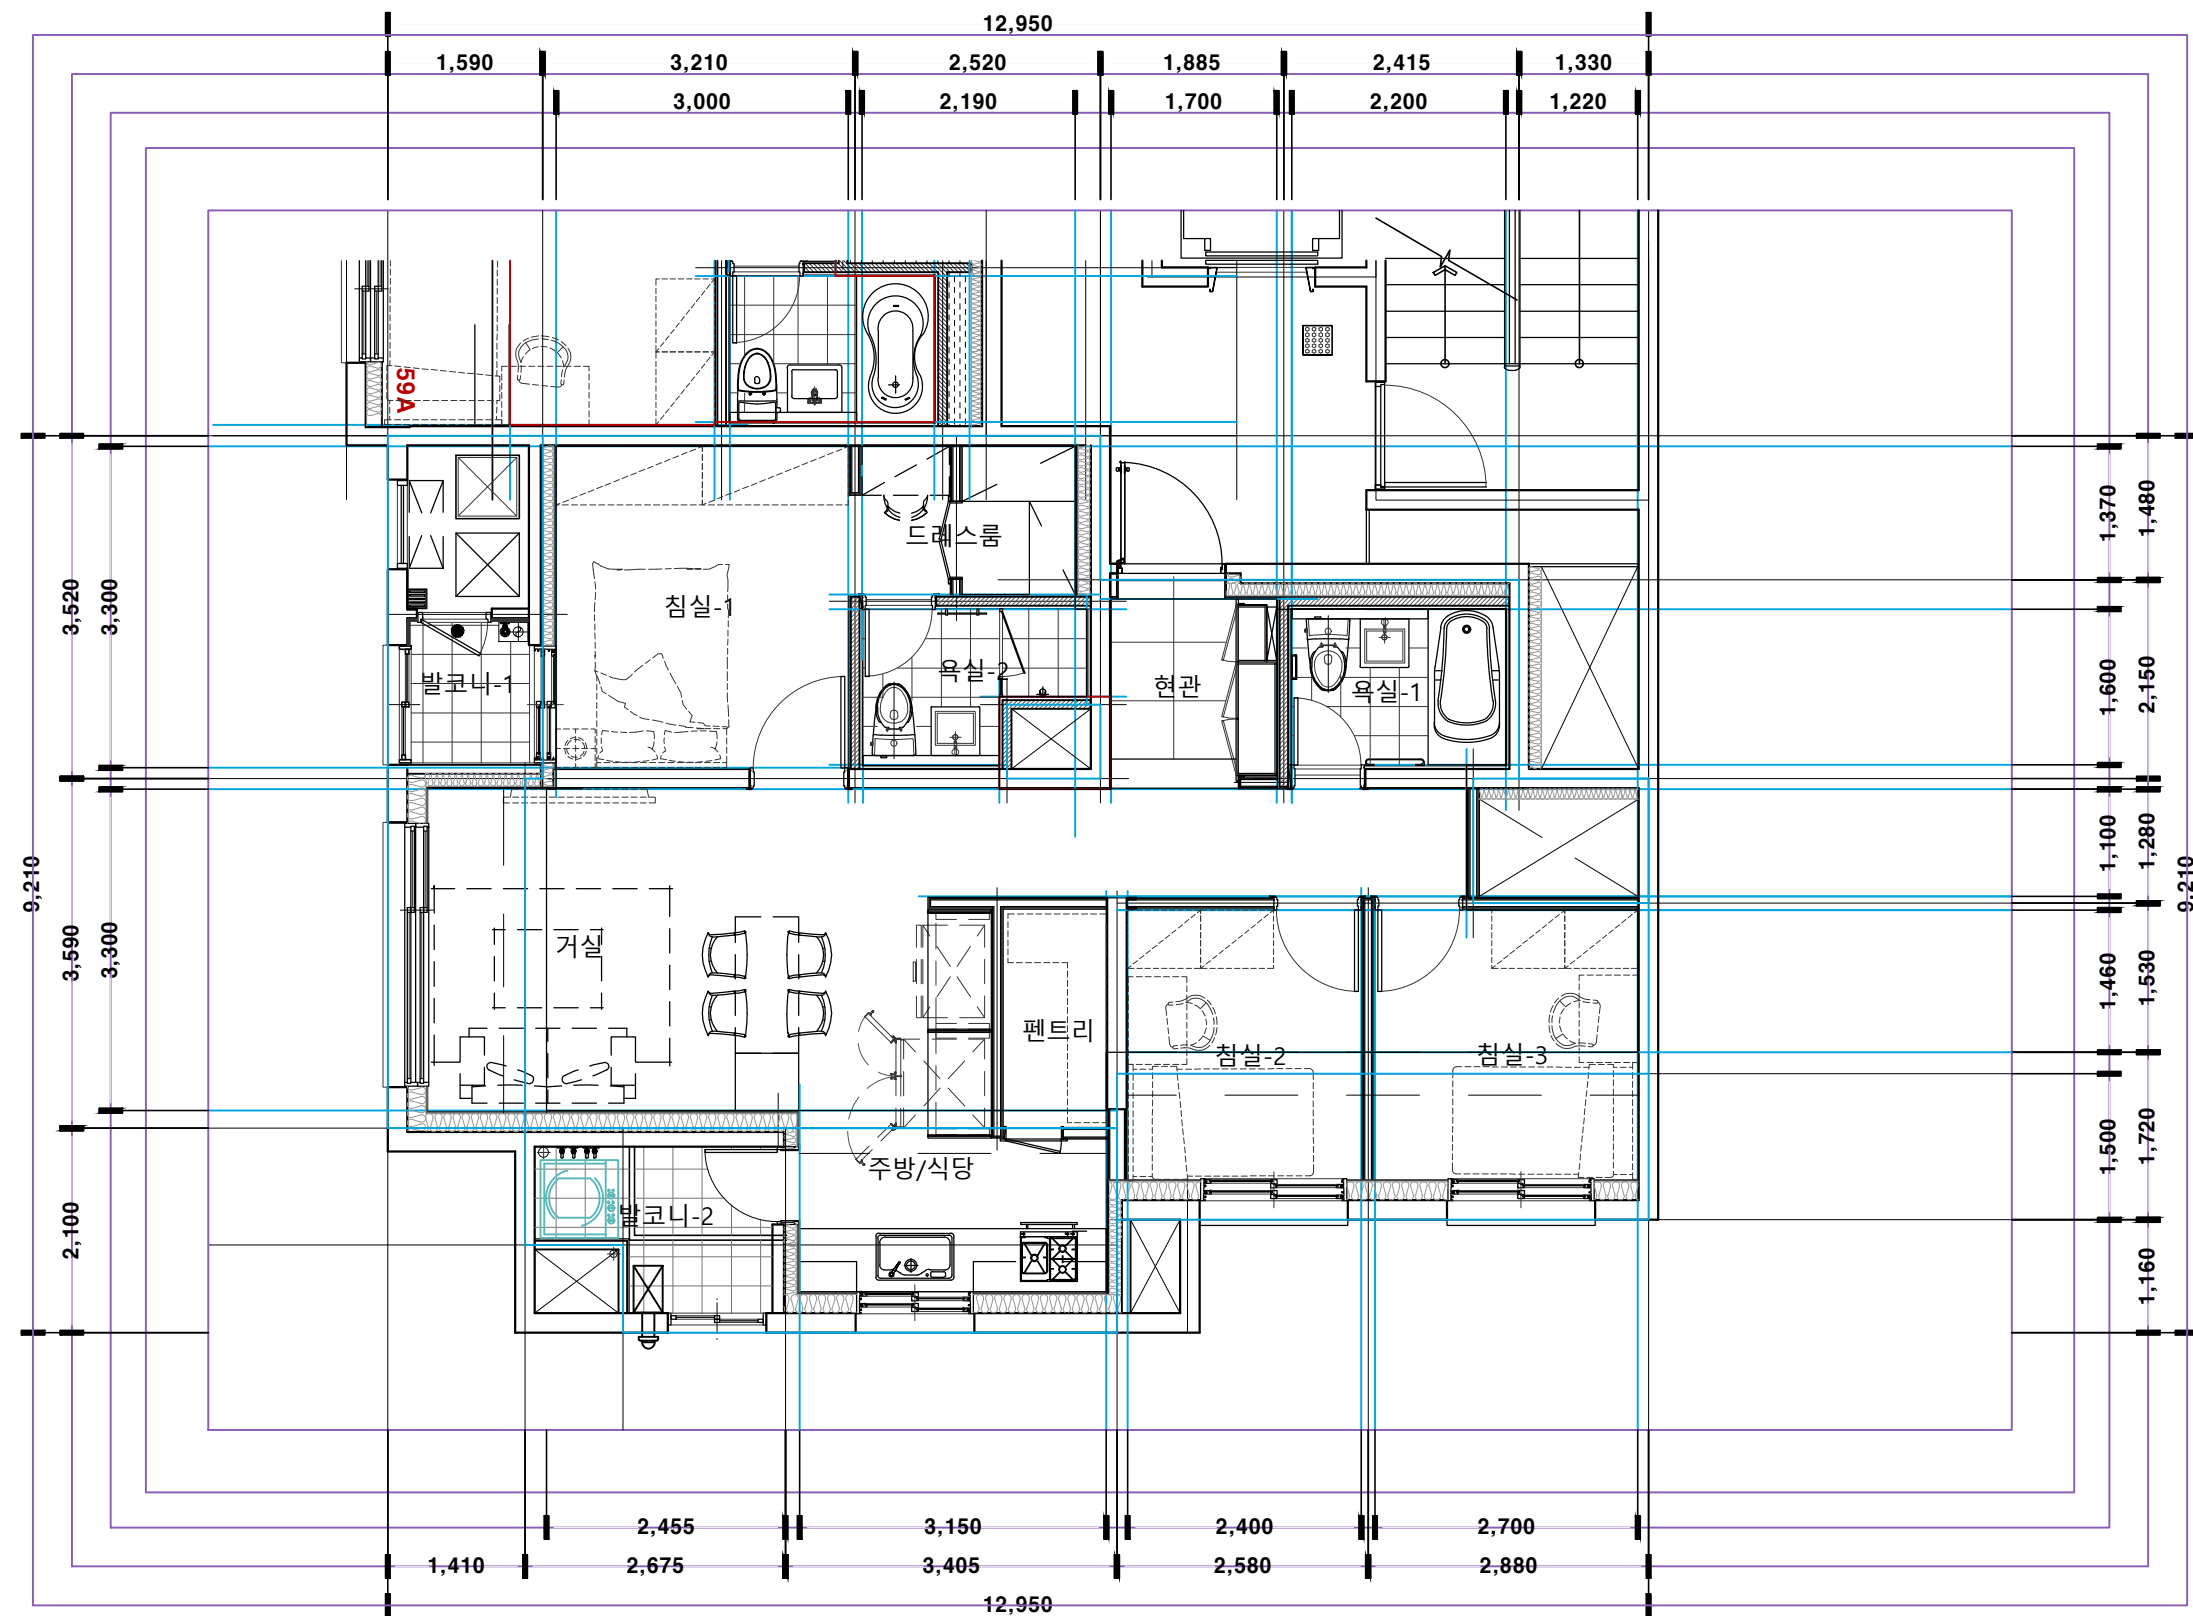


59B-단위세대평면도 SCALE : 1 / 80

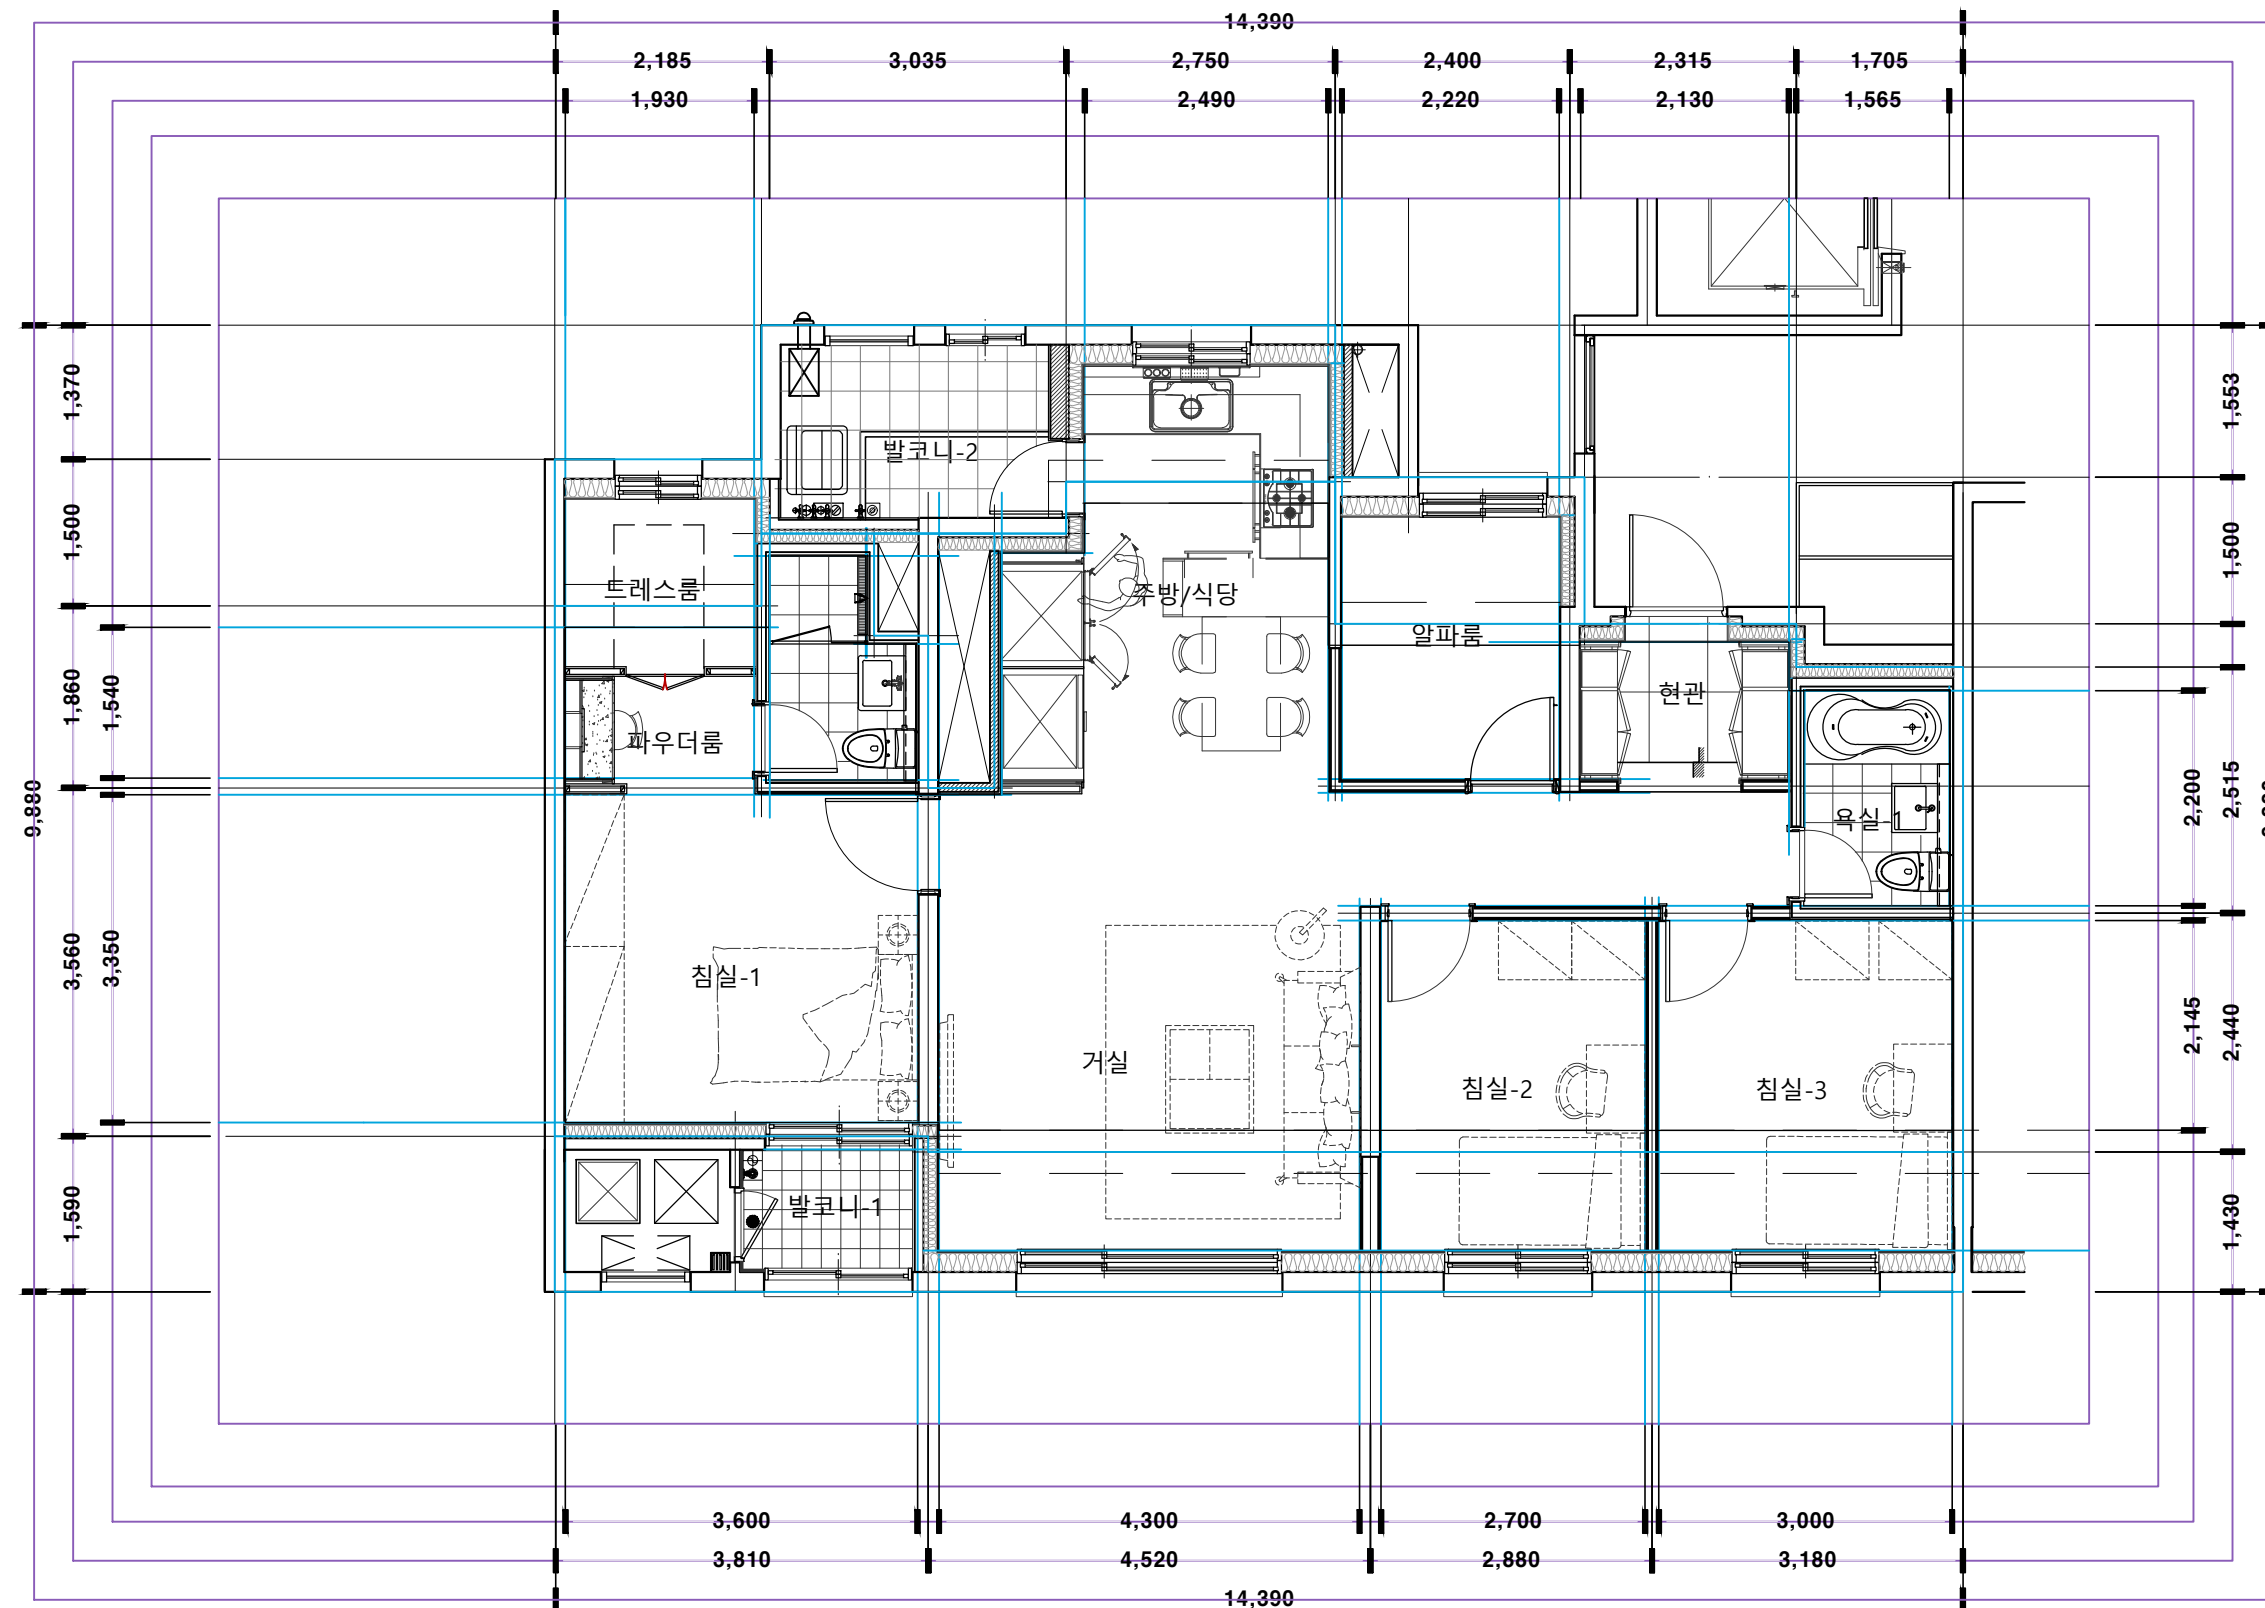


74A-단위세대평면도 SCALE : 1 / 80

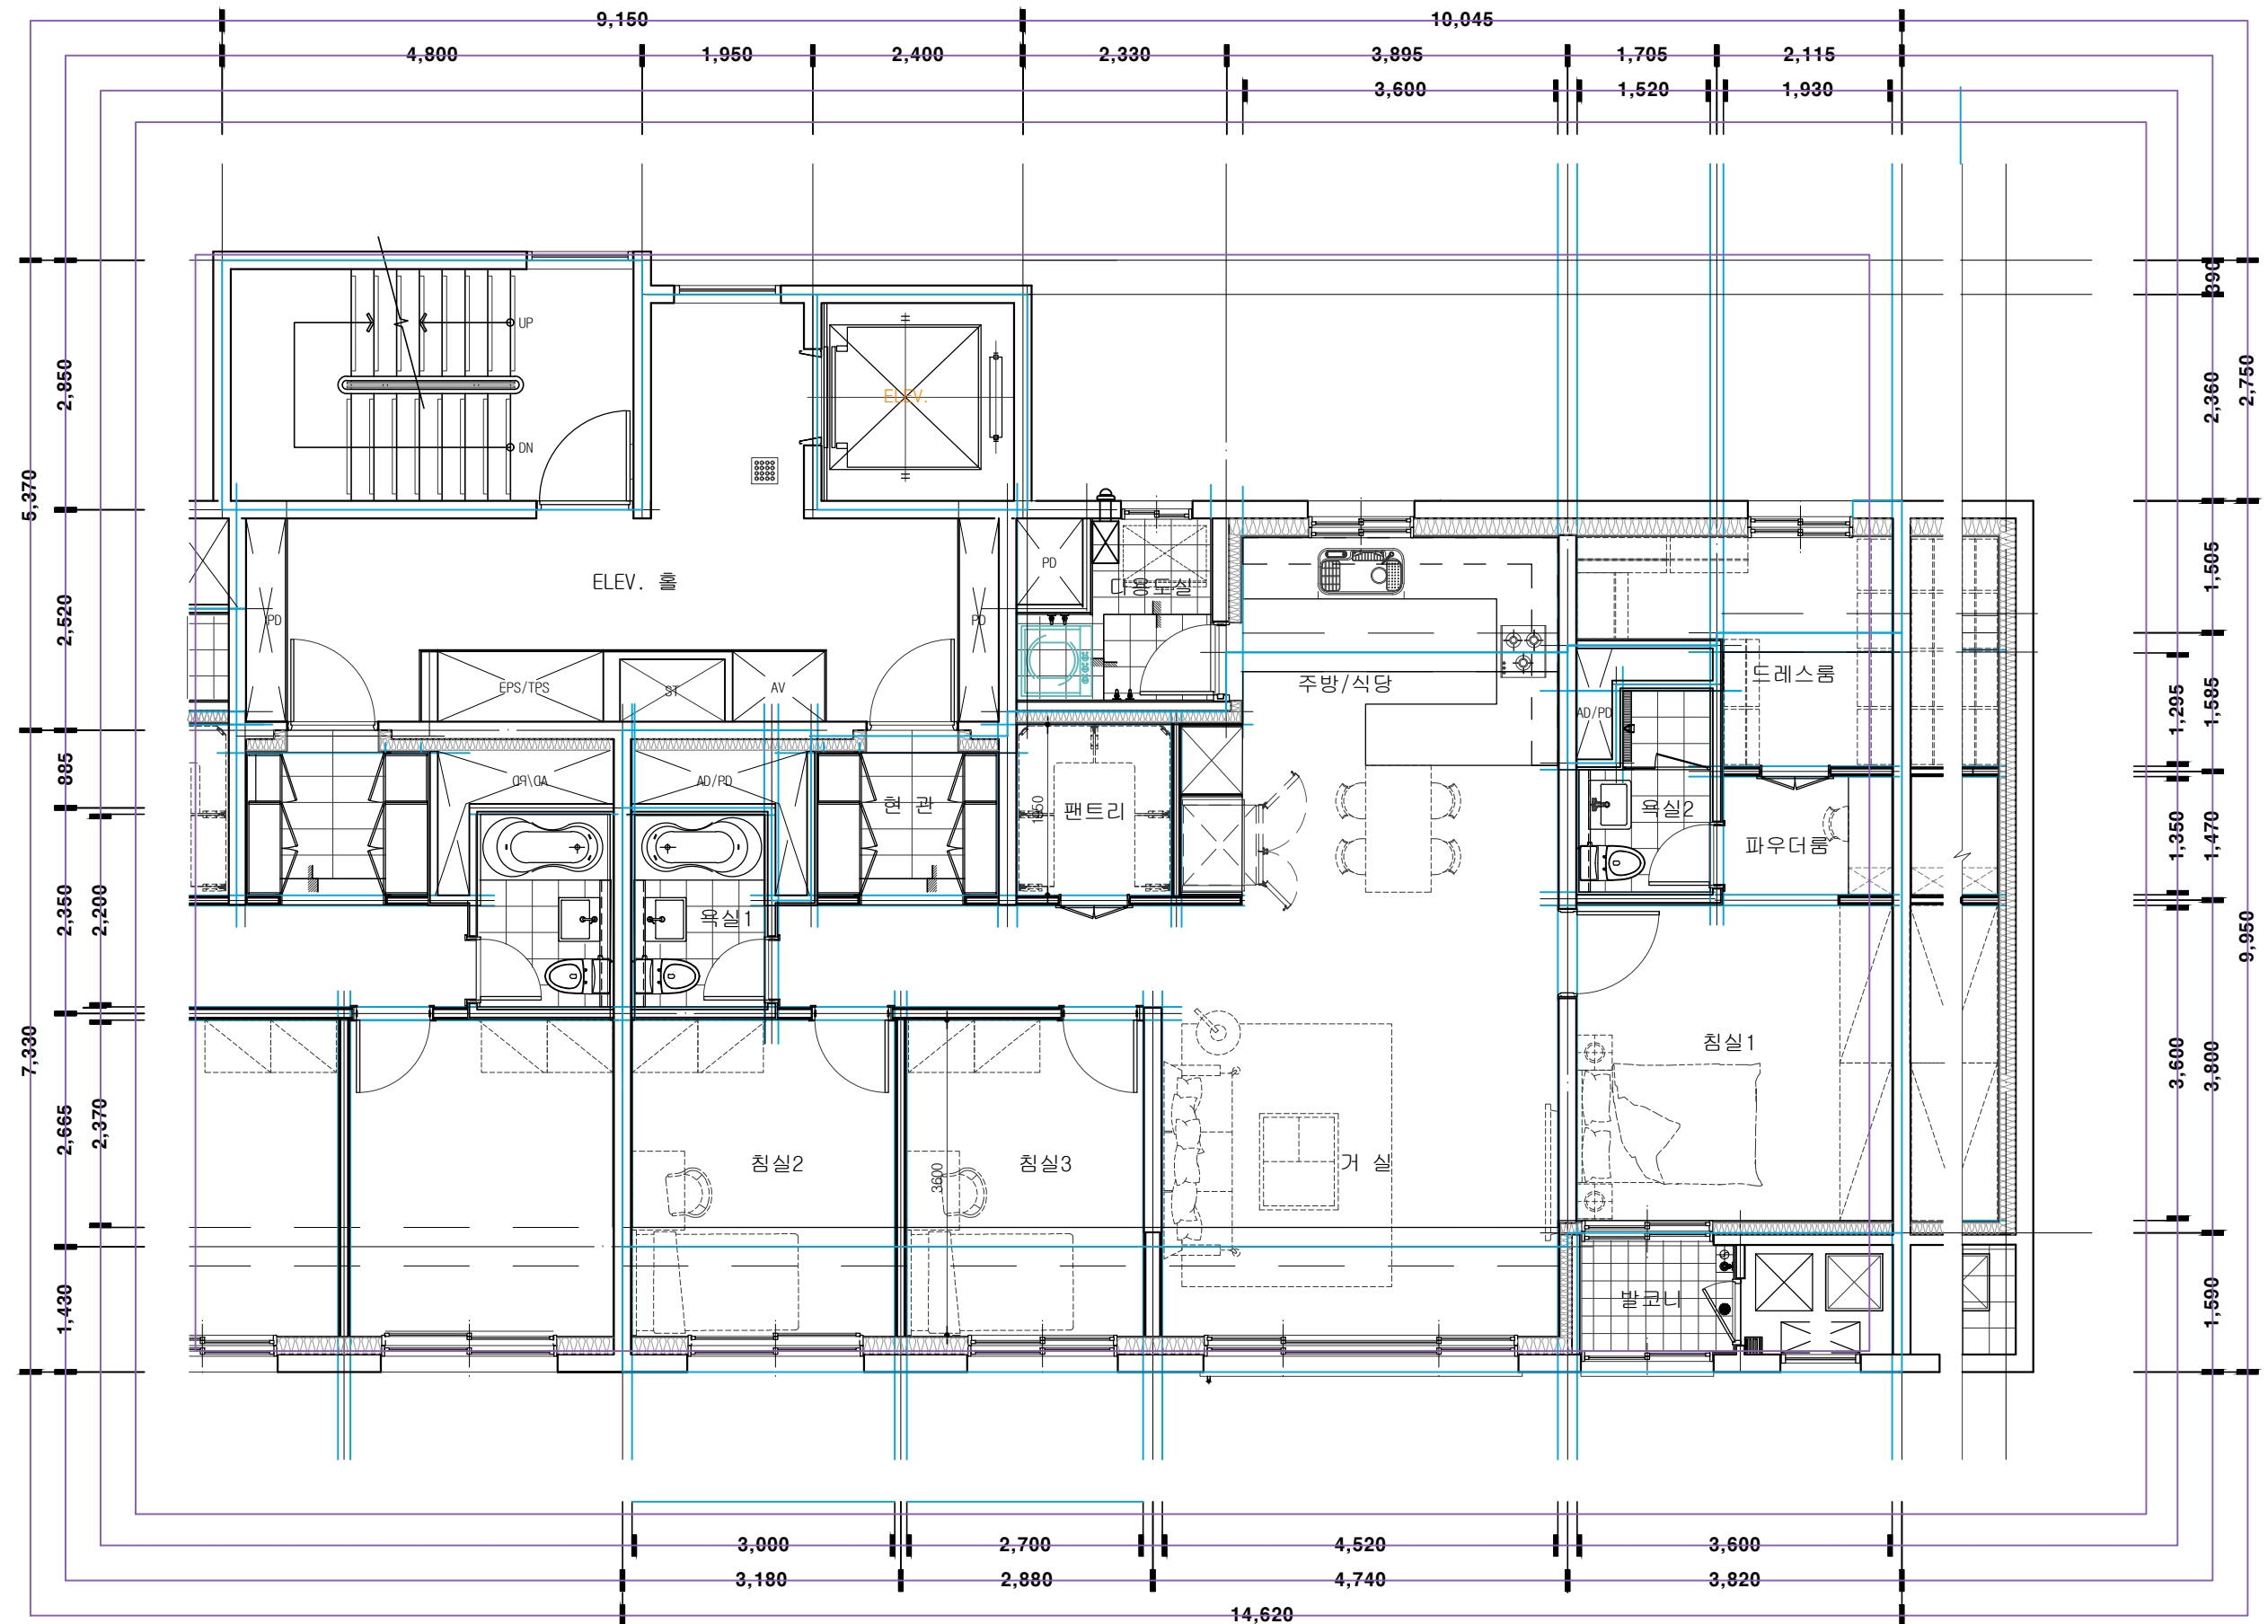

84A-단위세대평면도 SCALE : 1 / 80

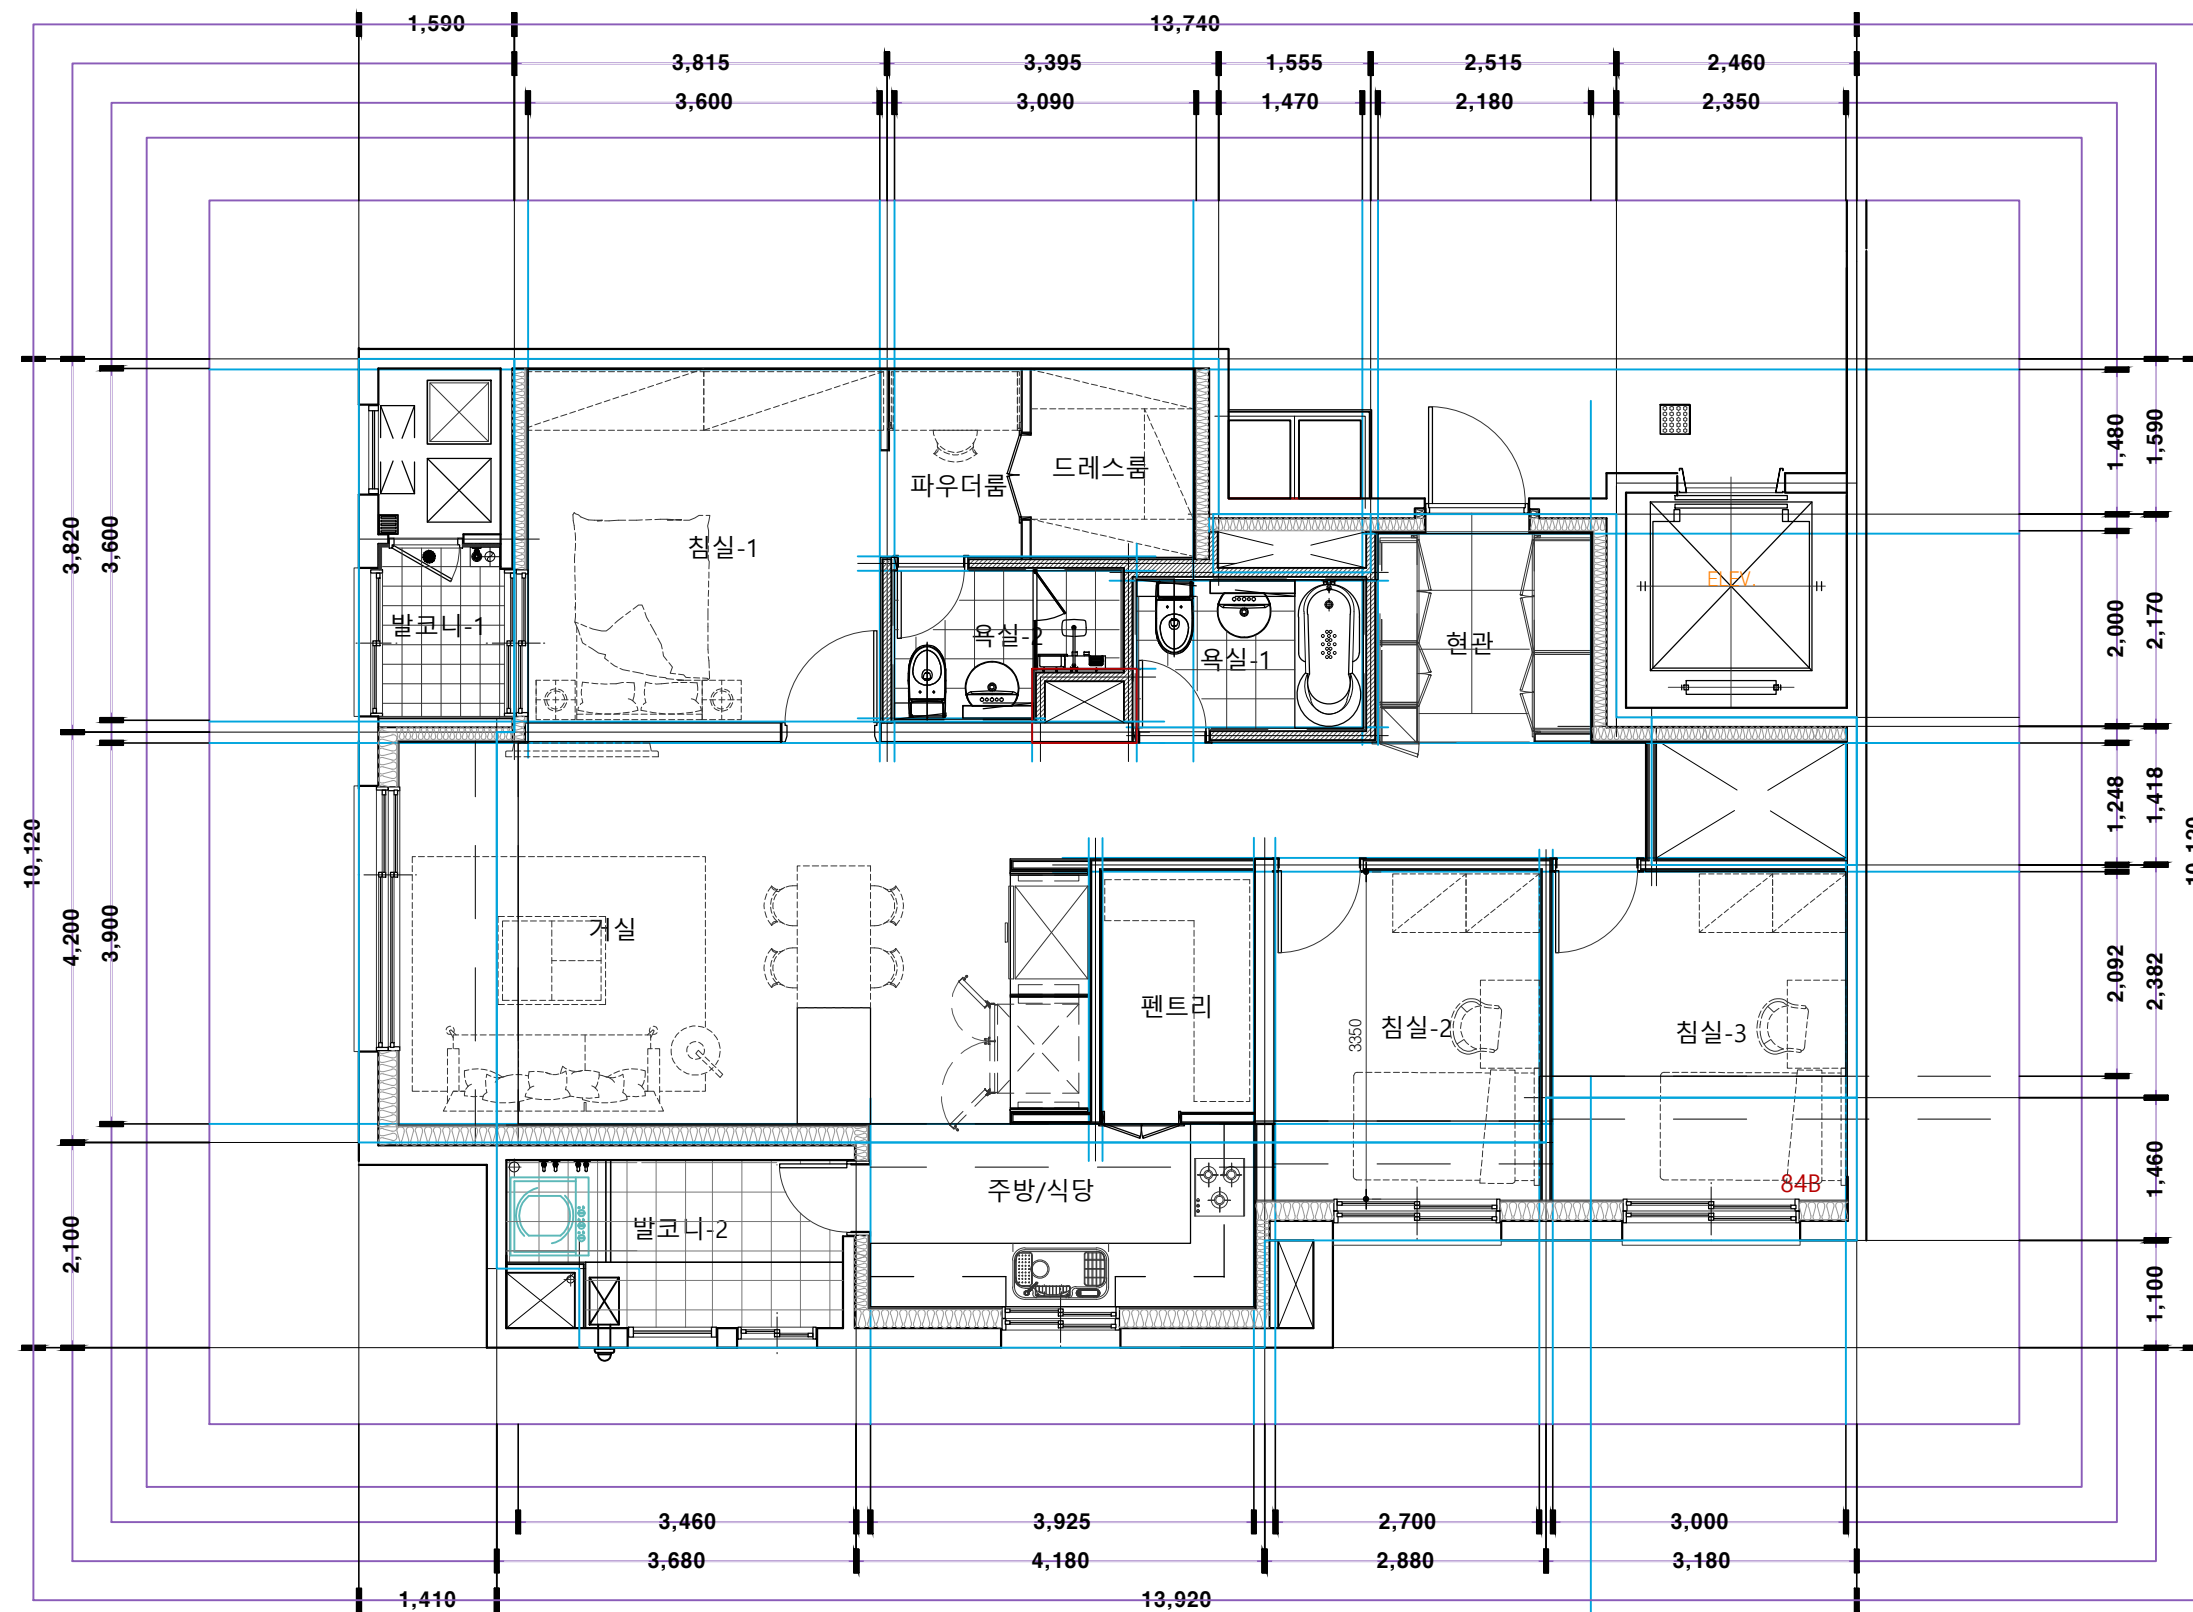

84B-단위세대평면도 SCALE : 1 / 80

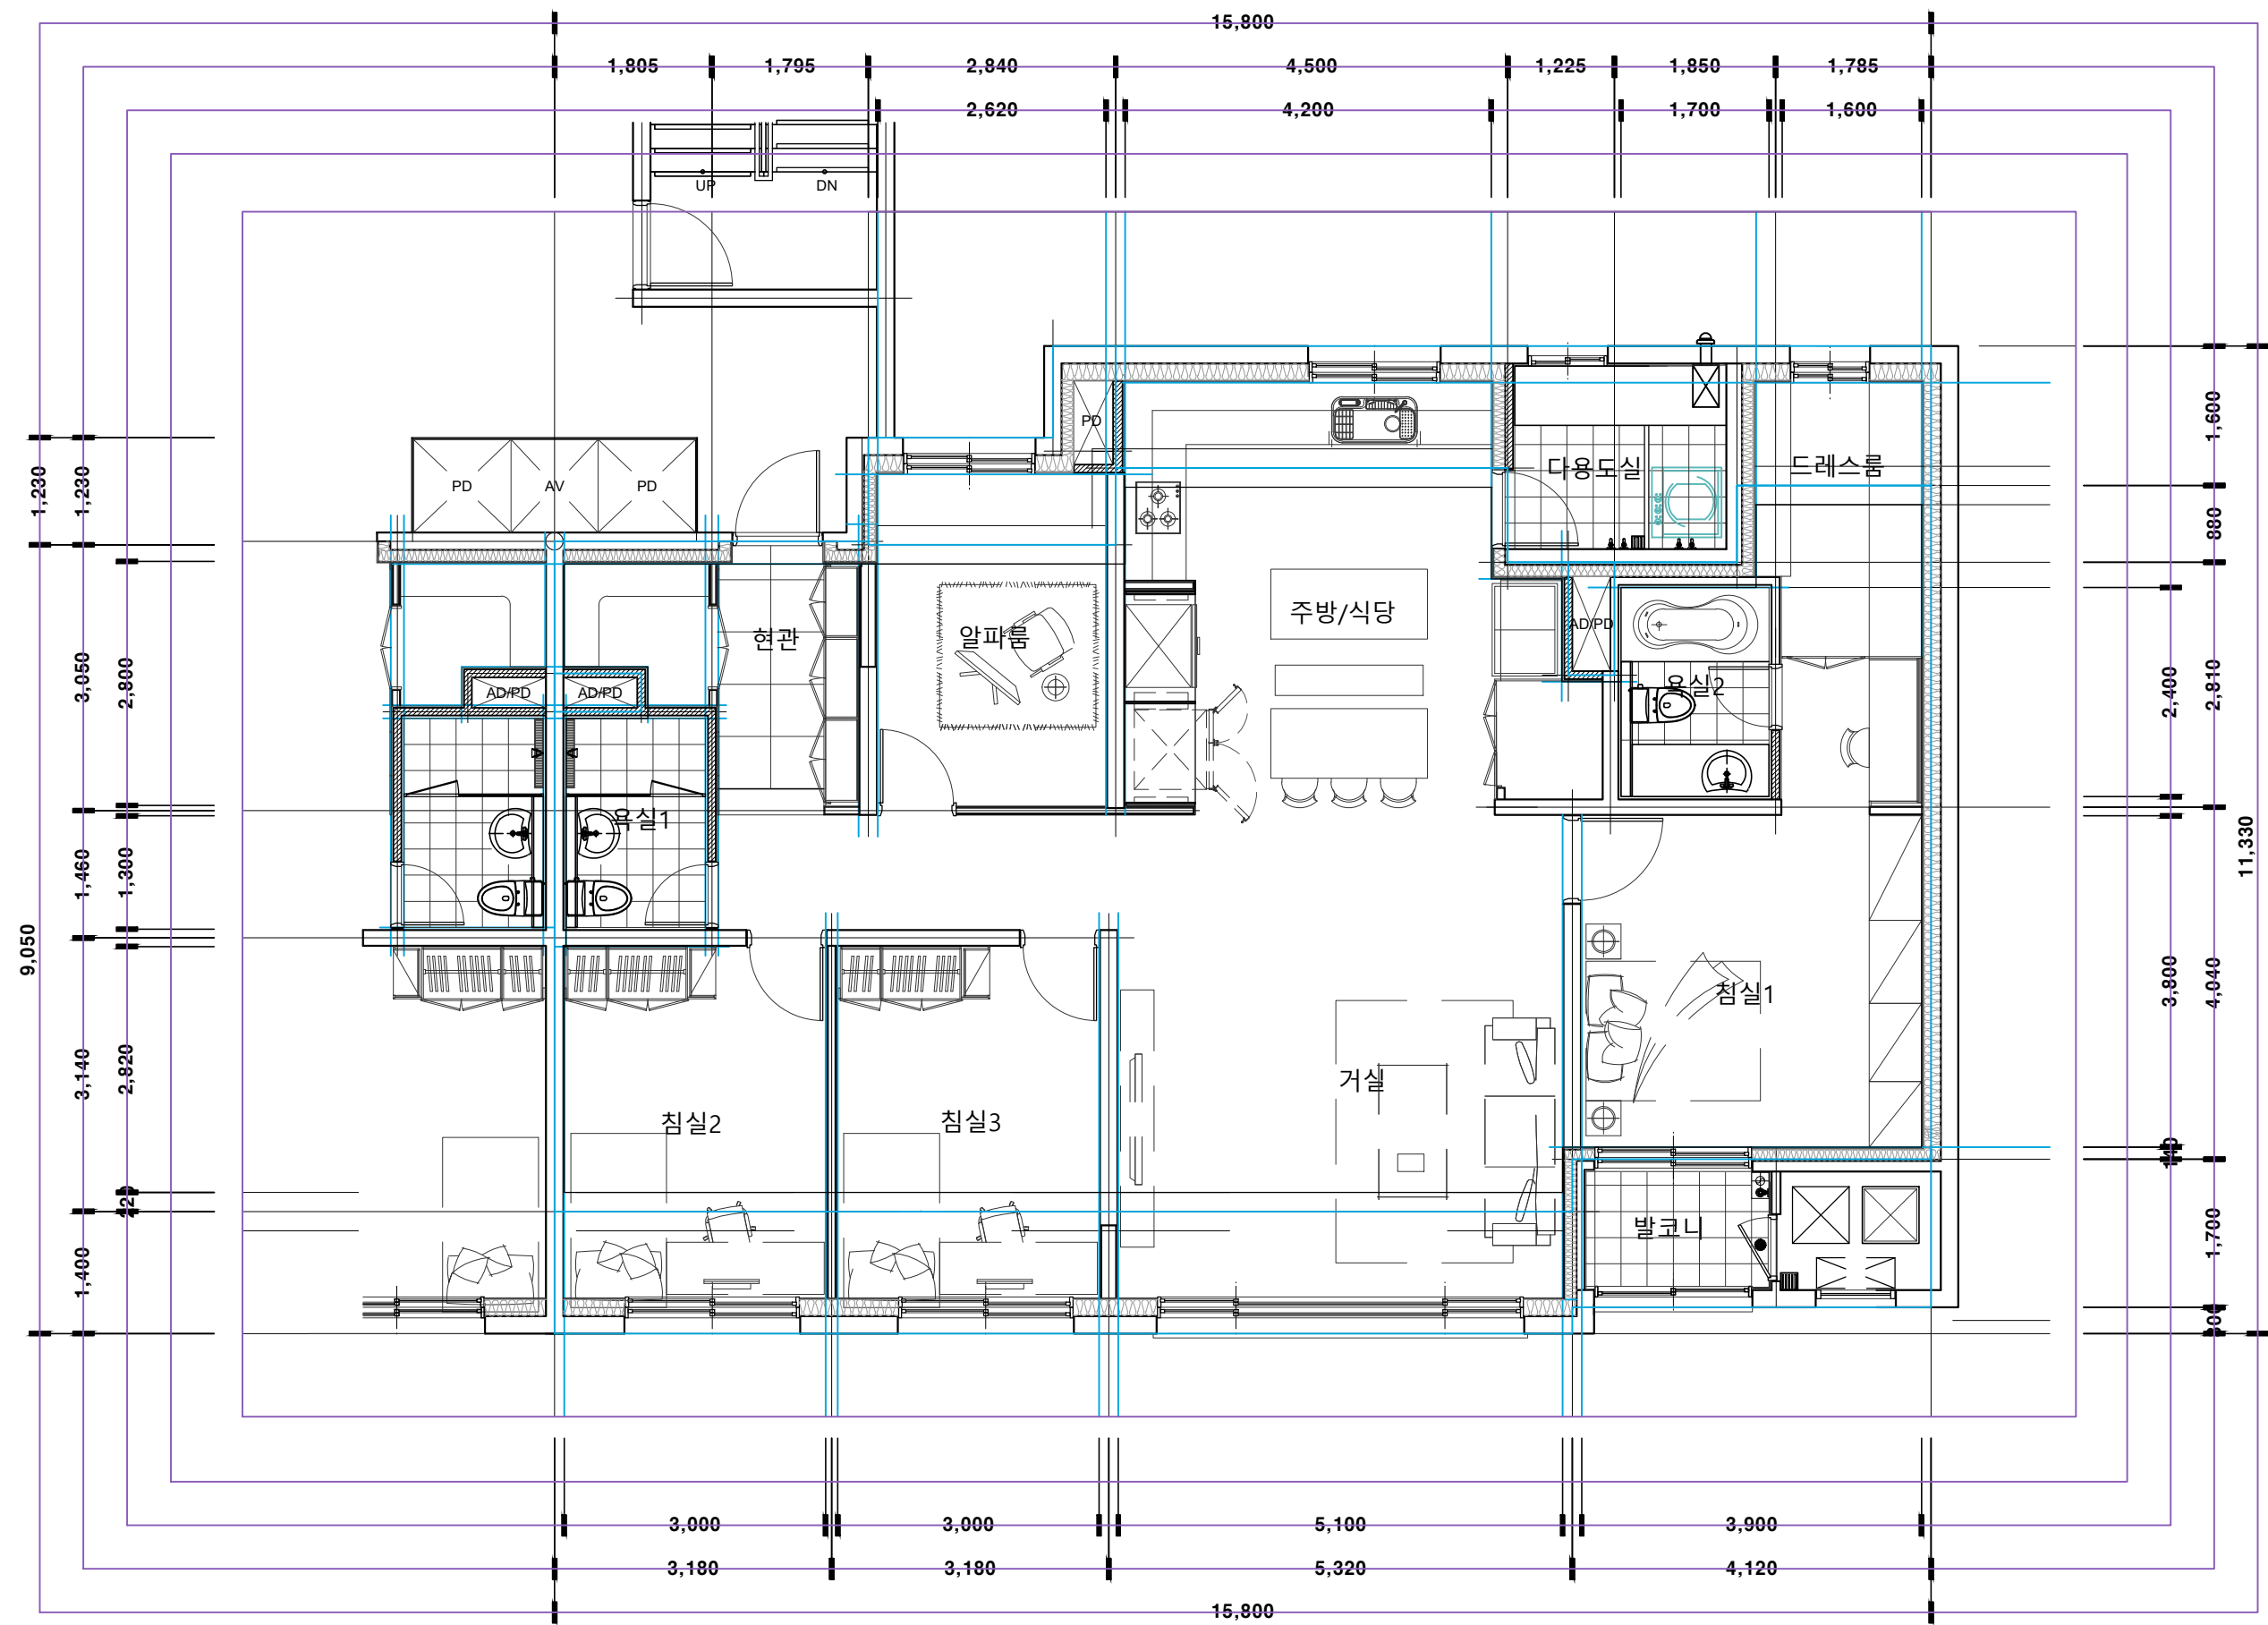

110 A-단위세대평면도 SCALE : 1 / 80